- 185" RAIL
- CUT-ONSITE RAIL
- #'- # #" - CUT-ONSITE RAIL LENGTH
- S5! ATTACHMENT
- S5! ATTACHMENT
- RAFTER @24"O.C.
- SPLICE BAR(TYP.)

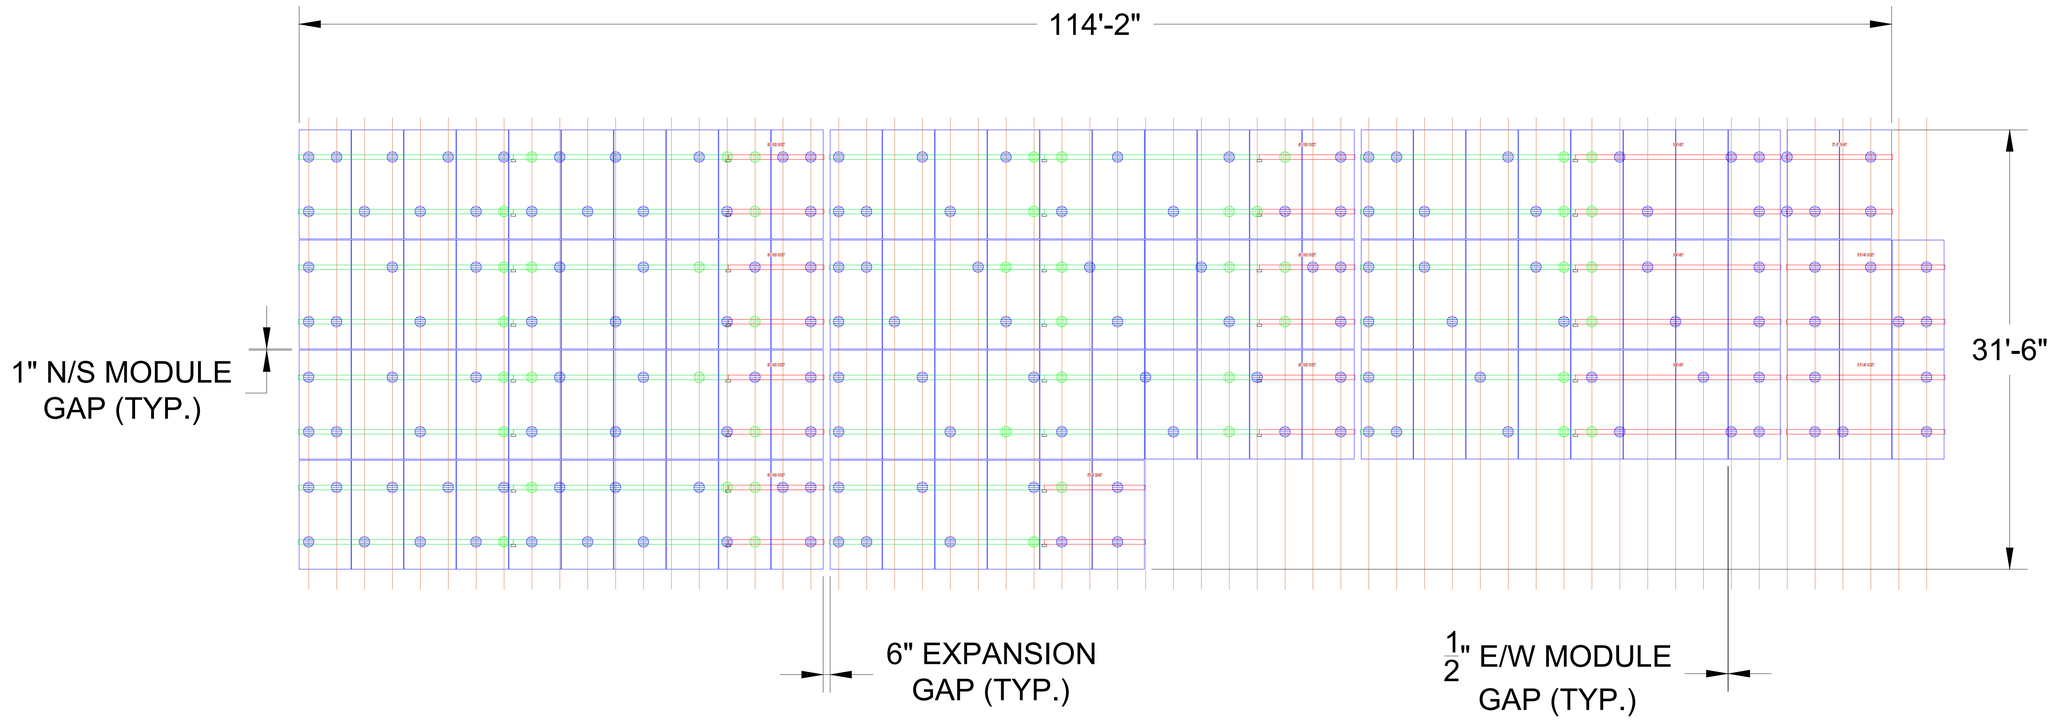

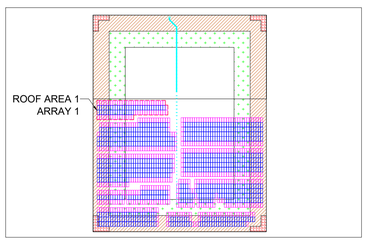

KEY PLAN
NOT TO SCALE

PLAN NORTH

NOT TO SCALE

ENGINEER'S STAMP

REVISIONS

REV	DATE	DESCRIPTION	DRW	CHK
0	01/27/2026	INITIAL RELEASE	MR	NT
A	02/02/2026	UPDATED PRODUCT	MR	NT
B	04/08/2026	UPDATED ATTACHMENT	SK	SK
-	-	-	-	-
-	-	-	-	-
-	-	-	-	-
-	-	-	-	-
-	-	-	-	-
-	-	-	-	-

FOR

PROJECT

TITLE

ARRAY LAYOUT
ROOF AREA 1
ARRAY 1

SHEET

SM.301

- 185" RAIL
- CUT-ONSITE RAIL
- #'- # #" - CUT-ONSITE RAIL LENGTH
- S5! ATTACHMENT
- S5! ATTACHMENT
- RAFTER @24"O.C.
- SPLICE BAR(TYP.)

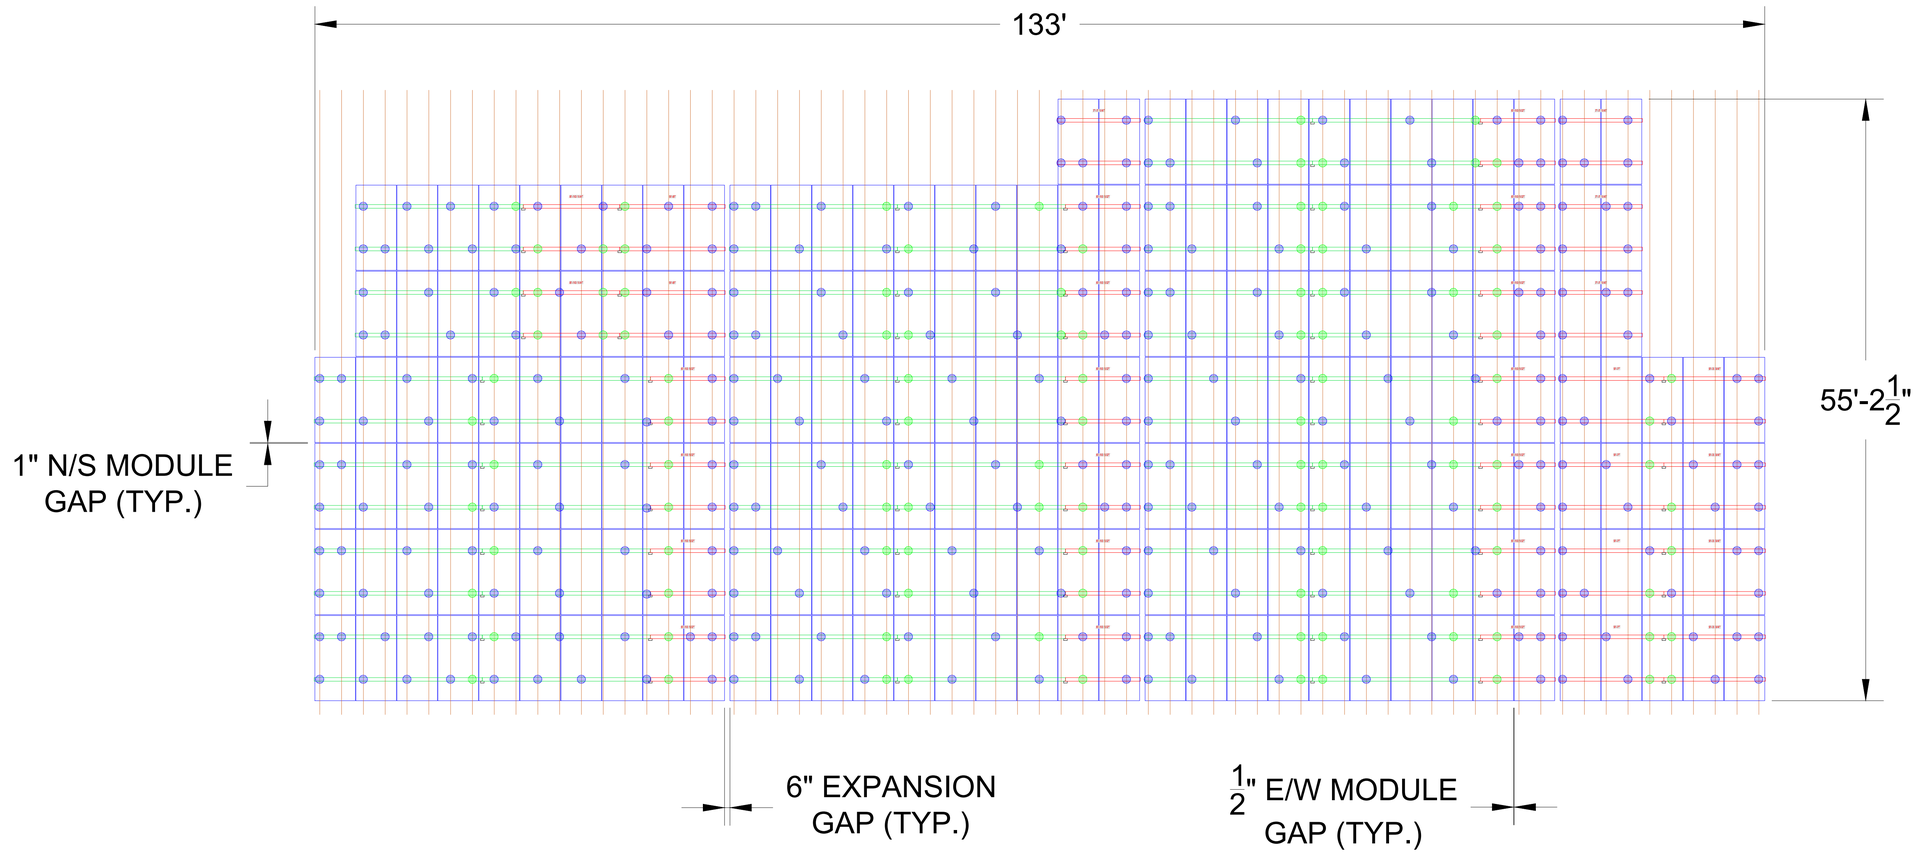

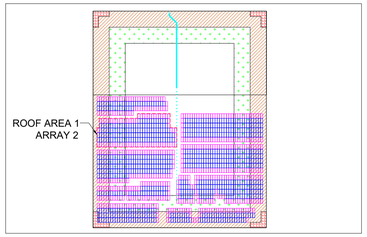

KEY PLAN
NOT TO SCALE

PLAN NORTH

NOT TO SCALE

ENGINEER'S STAMP

REVISIONS

REV	DATE	DESCRIPTION	DRW	CHK
0	01/27/2026	INITIAL RELEASE	MR	NT
A	02/02/2026	UPDATED PRODUCT	MR	NT
B	04/08/2026	UPDATED ATTACHMENT	SK	SK
-	-	-	-	-
-	-	-	-	-
-	-	-	-	-
-	-	-	-	-
-	-	-	-	-
-	-	-	-	-

FOR

PROJECT

TITLE

ARRAY LAYOUT
ROOF AREA 1
ARRAY 1

SHEET

SM.302

- 185" RAIL
- CUT-ONSITE RAIL
- #'- # #" - CUT-ONSITE RAIL LENGTH
- S5! ATTACHMENT
- S5! ATTACHMENT
- RAFTER @24"O.C.
- SPLICE BAR(TYP.)

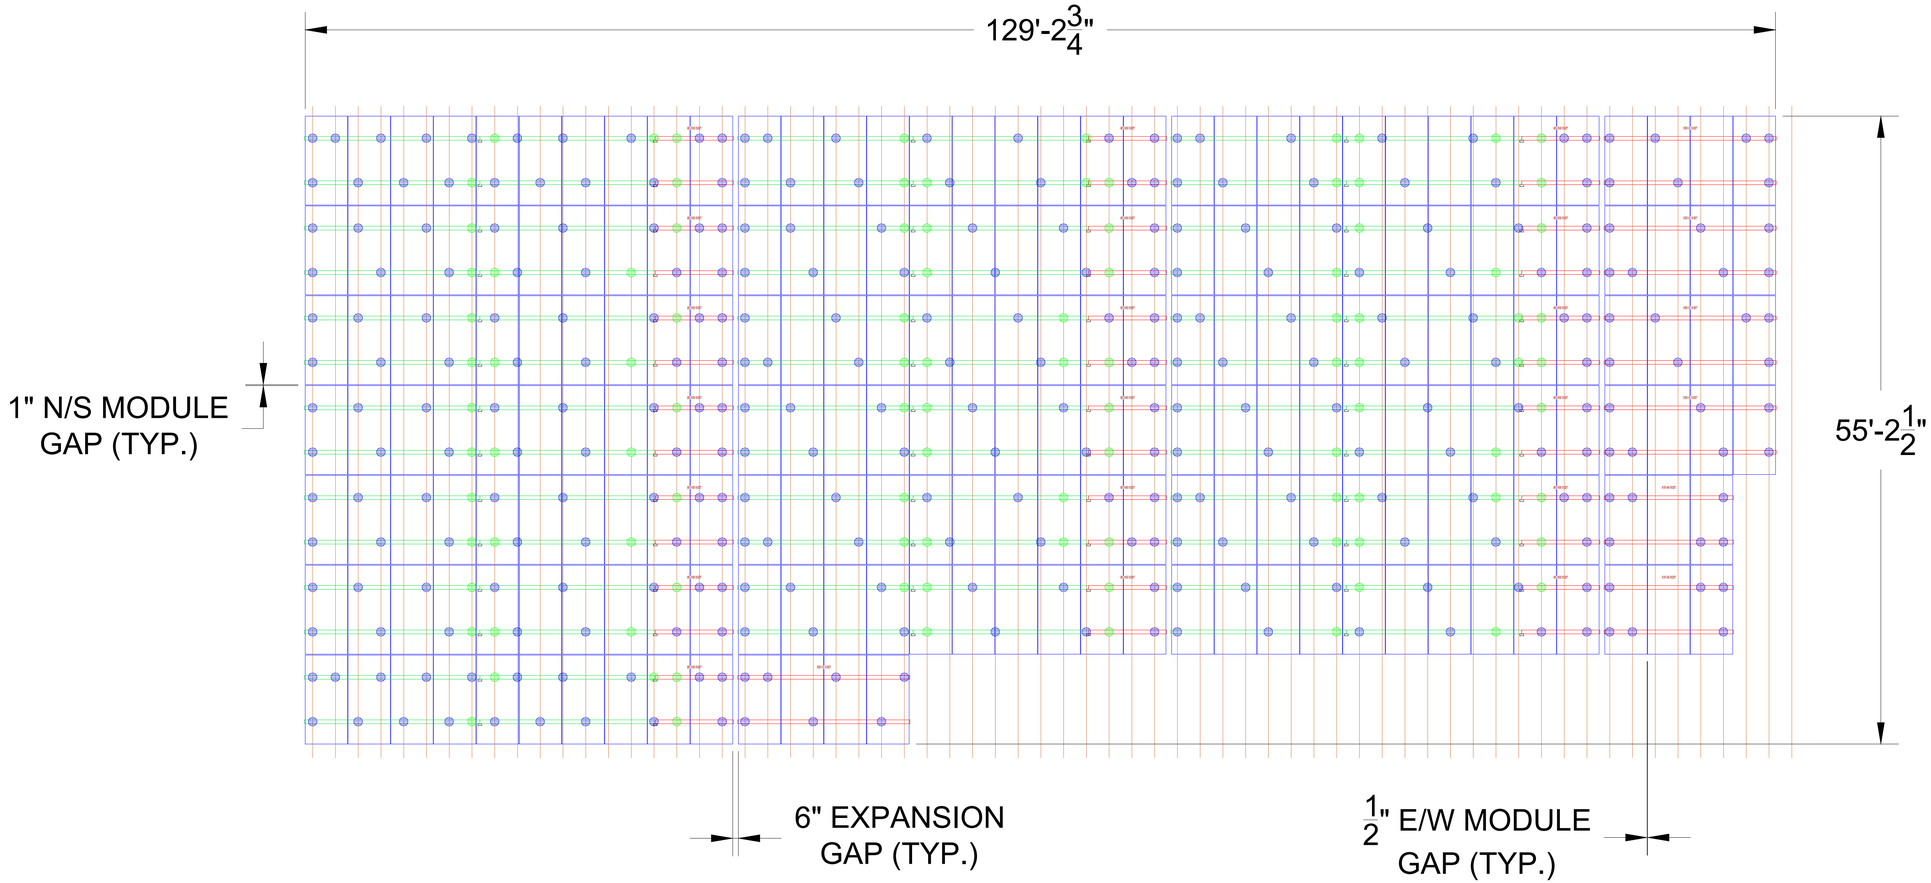

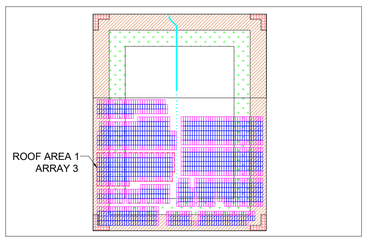

KEY PLAN
NOT TO SCALE

PLAN NORTH

NOT TO SCALE

ENGINEER'S STAMP

REVISIONS

REV	DATE	DESCRIPTION	DRW	CHK
0	01/27/2026	INITIAL RELEASE	MR	NT
A	02/02/2026	UPDATED PRODUCT	MR	NT
B	04/08/2026	UPDATED ATTACHMENT	SK	SK
-	-	-	-	-
-	-	-	-	-
-	-	-	-	-
-	-	-	-	-
-	-	-	-	-
-	-	-	-	-

FOR

PROJECT

TITLE

ARRAY LAYOUT
ROOF AREA 1
ARRAY 3

SHEET

SM.303

- 185" RAIL
- CUT-ONSITE RAIL
- #'- # #" - CUT-ONSITE RAIL LENGTH
- S5! ATTACHMENT
- S5! ATTACHMENT
- RAFTER @24"O.C.
- SPLICE BAR(TYP.)

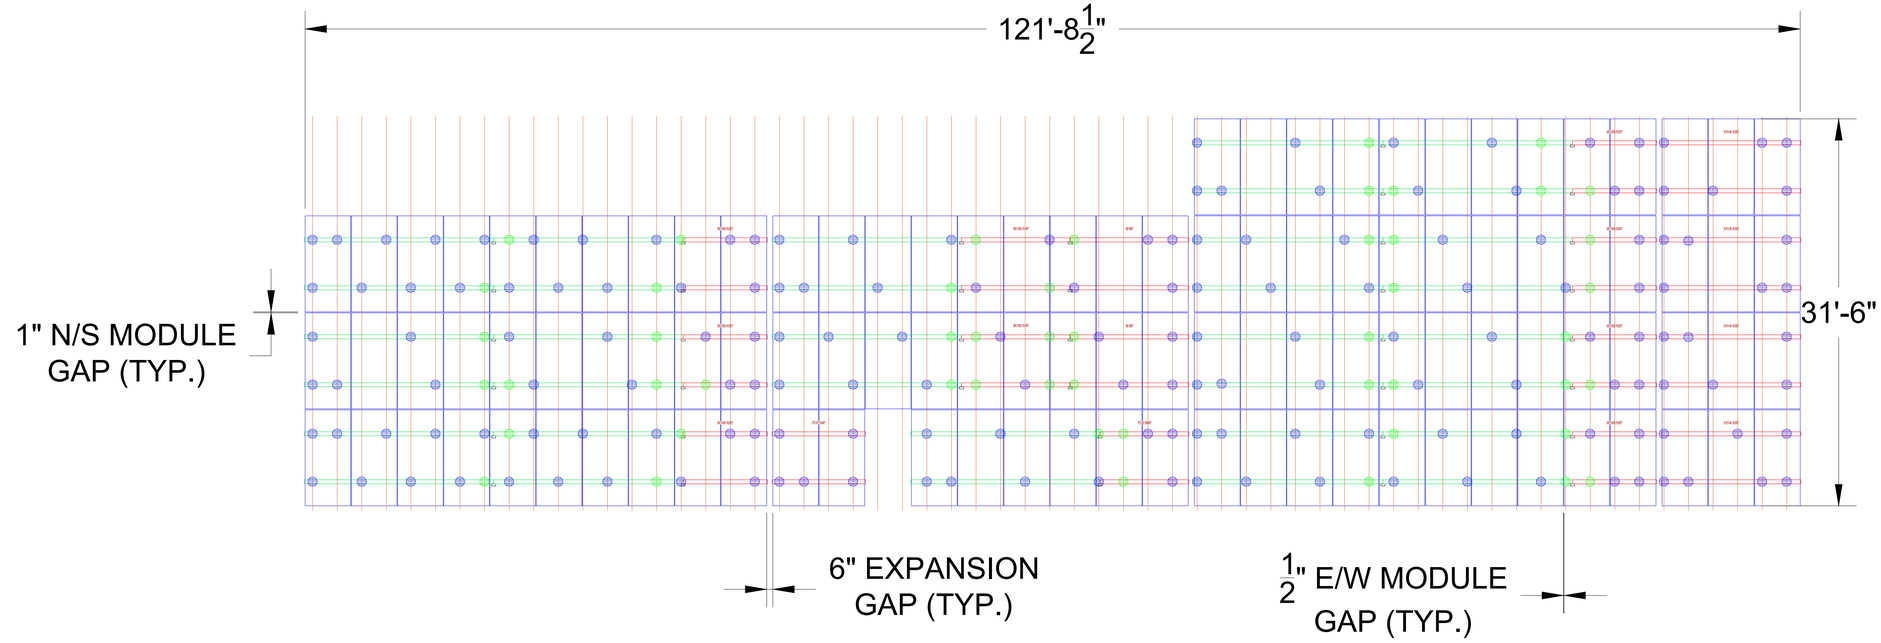

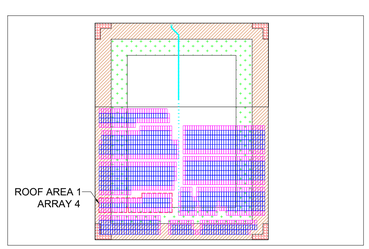

KEY PLAN
NOT TO SCALE

PLAN NORTH

NOT TO SCALE

ENGINEER'S STAMP

REVISIONS

REV	DATE	DESCRIPTION	DRW	CHK
0	01/27/2026	INITIAL RELEASE	MR	NT
A	02/02/2026	UPDATED PRODUCT	MR	NT
B	04/08/2026	UPDATED ATTACHMENT	SK	SK
-	-	-	-	-
-	-	-	-	-
-	-	-	-	-
-	-	-	-	-
-	-	-	-	-
-	-	-	-	-

FOR

PROJECT

TITLE

ARRAY LAYOUT
ROOF AREA 1
ARRAY 40

SHEET

SM.304

- 185" RAIL
- CUT-ONSITE RAIL
- #'- # #" - CUT-ONSITE RAIL LENGTH
- S5! ATTACHMENT
- S5! ATTACHMENT
- RAFTER @24"O.C.
- SPLICE BAR(TYP.)

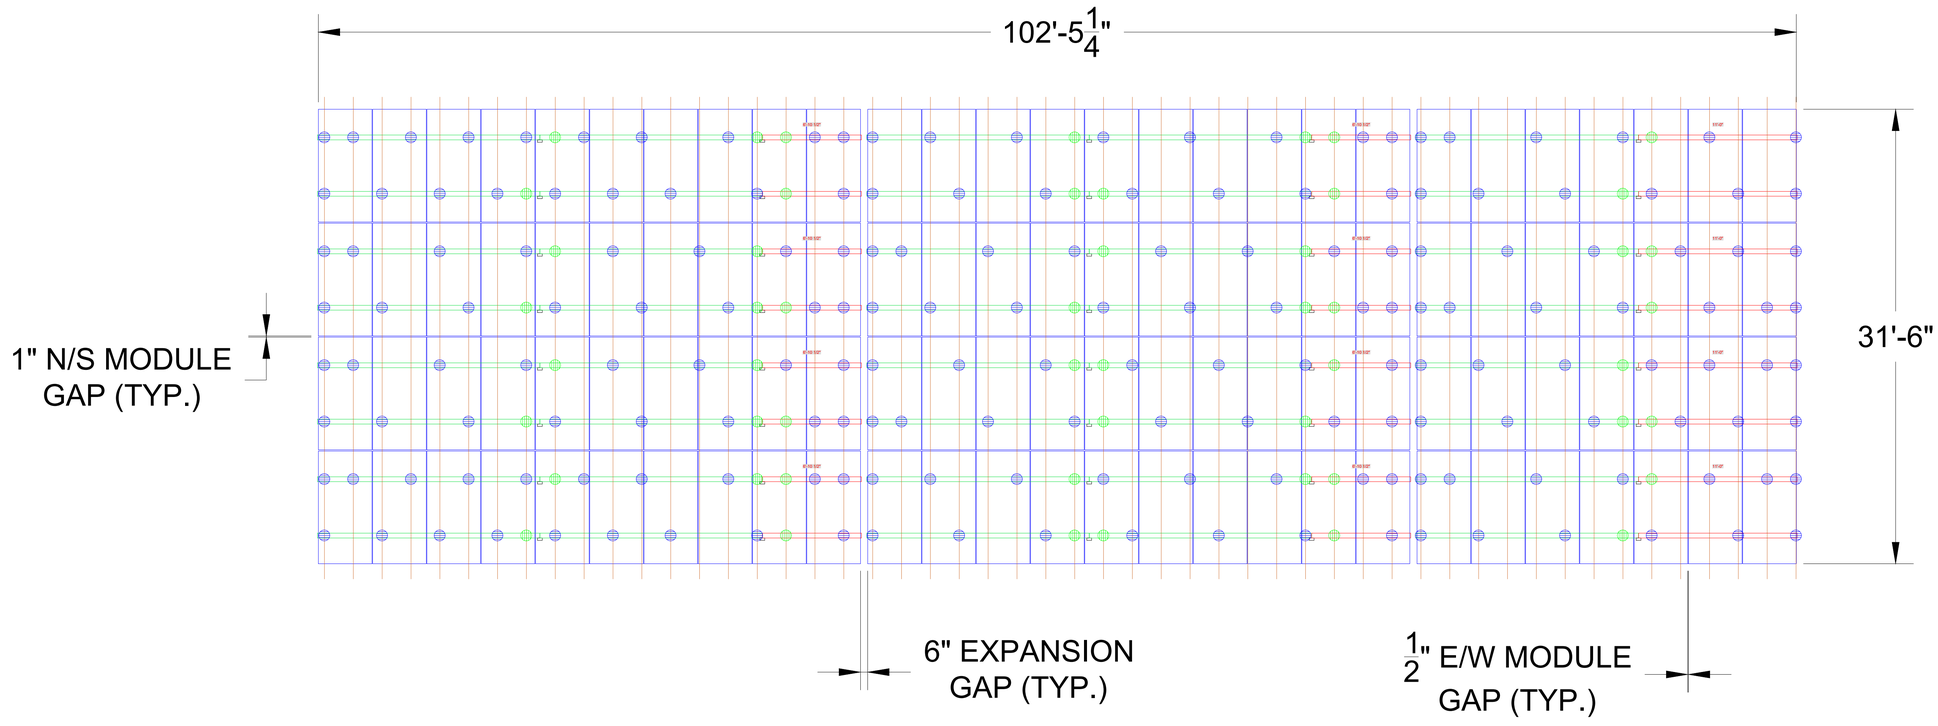

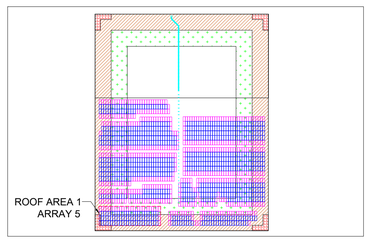

KEY PLAN
NOT TO SCALE

NOT TO SCALE

ENGINEER'S STAMP

REVISIONS

REV	DATE	DESCRIPTION	DRW	CHK
0	01/27/2026	INITIAL RELEASE	MR	NT
A	02/02/2026	UPDATED PRODUCT	MR	NT
B	04/08/2026	UPDATED ATTACHMENT	SK	SK
-	-	-	-	-
-	-	-	-	-
-	-	-	-	-
-	-	-	-	-
-	-	-	-	-
-	-	-	-	-

FOR

PROJECT

TITLE

ARRAY LAYOUT
ROOF AREA 1
ARRAY 66

SHEET

SM.305

- 185" RAIL
- CUT-ONSITE RAIL
- #'- # #" - CUT-ONSITE RAIL LENGTH
- S5! ATTACHMENT
- S5! ATTACHMENT
- RAFTER @24"O.C.
- SPLICE BAR(TYP.)

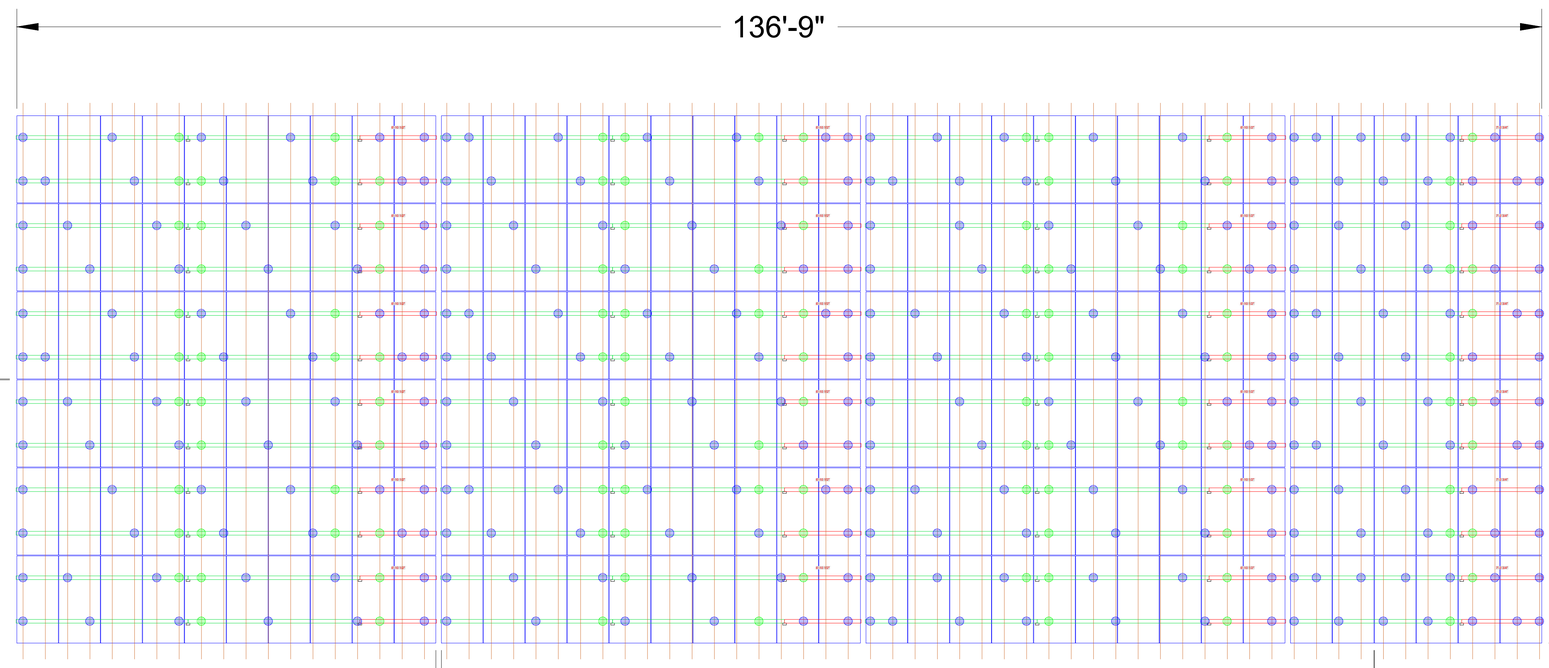

1" N/S MODULE GAP (TYP.)

6" EXPANSION GAP (TYP.)

1/2" E/W MODULE GAP (TYP.)

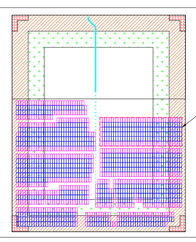

KEY PLAN
NOT TO SCALE

PLAN NORTH

NOT TO SCALE

ENGINEER'S STAMP

REVISIONS

REV	DATE	DESCRIPTION	DRW	CHK
0	01/27/2026	INITIAL RELEASE	MR	NT
A	02/02/2026	UPDATED PRODUCT	MR	NT
B	04/08/2026	UPDATED ATTACHMENT	SK	SK
-	-	-	-	-
-	-	-	-	-
-	-	-	-	-
-	-	-	-	-
-	-	-	-	-
-	-	-	-	-

FOR

PROJECT

TITLE

ARRAY LAYOUT
ROOF AREA 1
ARRAY 6

SHEET

SM.306

- 185" RAIL
- CUT-ONSITE RAIL
- #'- # #" - CUT-ONSITE RAIL LENGTH
- S5! ATTACHMENT
- S5! ATTACHMENT
- RAFTER @24"O.C.
- SPLICE BAR(TYP.)

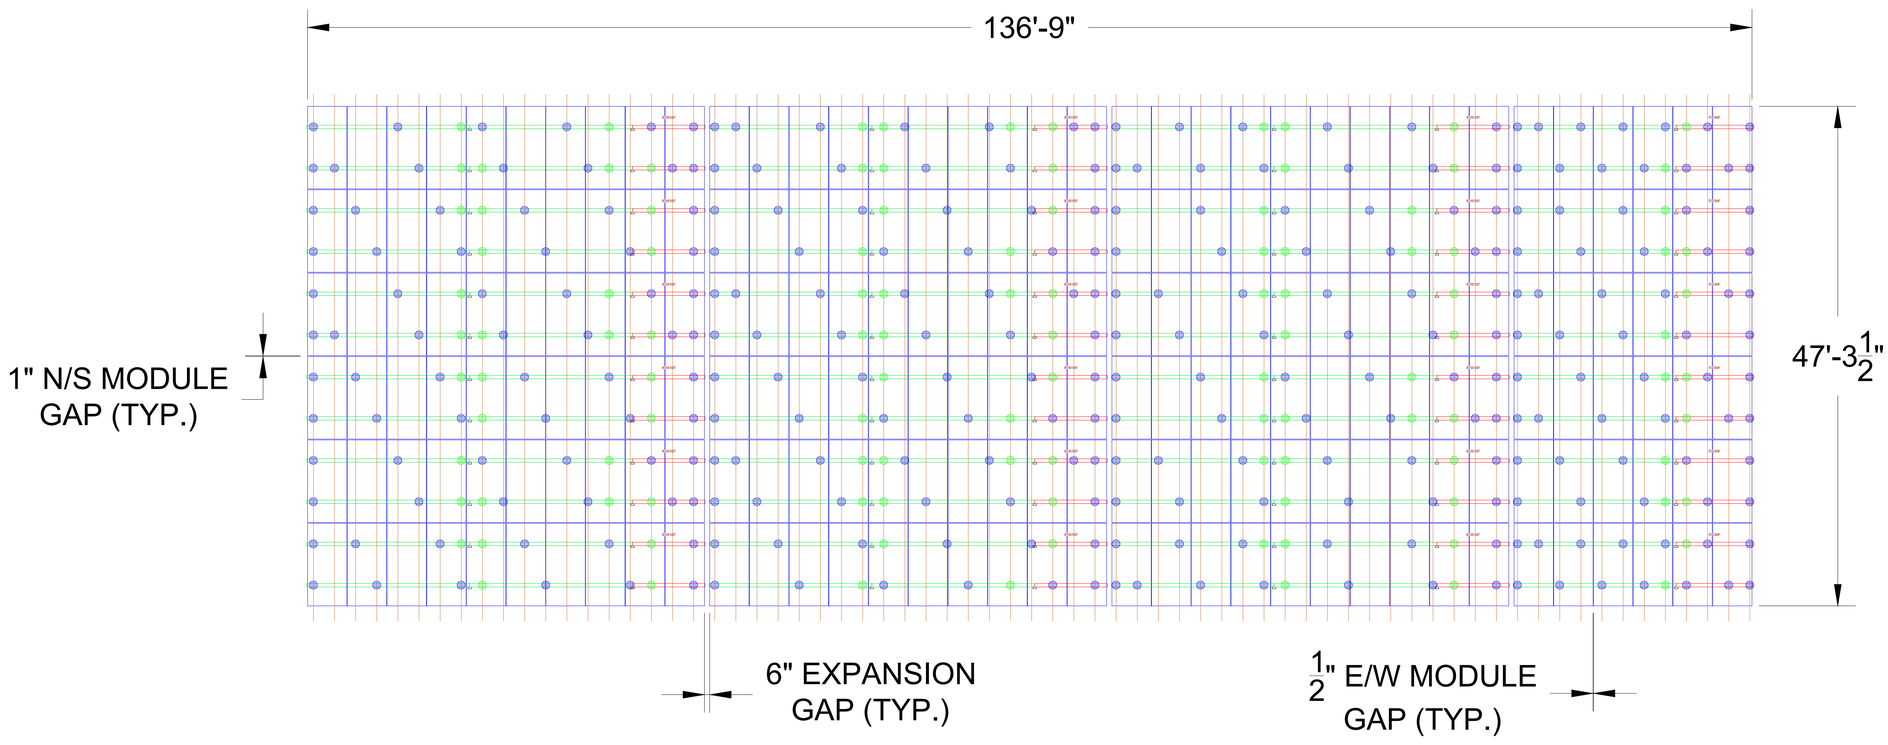

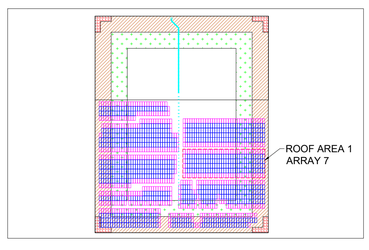

KEY PLAN
NOT TO SCALE

PLAN NORTH

NOT TO SCALE

ENGINEER'S STAMP

REVISIONS

REV	DATE	DESCRIPTION	DRW	CHK
0	01/27/2026	INITIAL RELEASE	MR	NT
A	02/02/2026	UPDATED PRODUCT	MR	NT
B	04/08/2026	UPDATED ATTACHMENT	SK	SK
-	-	-	-	-
-	-	-	-	-
-	-	-	-	-
-	-	-	-	-
-	-	-	-	-
-	-	-	-	-

FOR

PROJECT

TITLE

ARRAY LAYOUT
ROOF AREA 1
ARRAY 5

SHEET

SM.307

- 185" RAIL
- CUT-ONSITE RAIL
- #'- # #" - CUT-ONSITE RAIL LENGTH
- S5! ATTACHMENT
- S5! ATTACHMENT
- RAFTER @24"O.C.
- SPLICE BAR(TYP.)

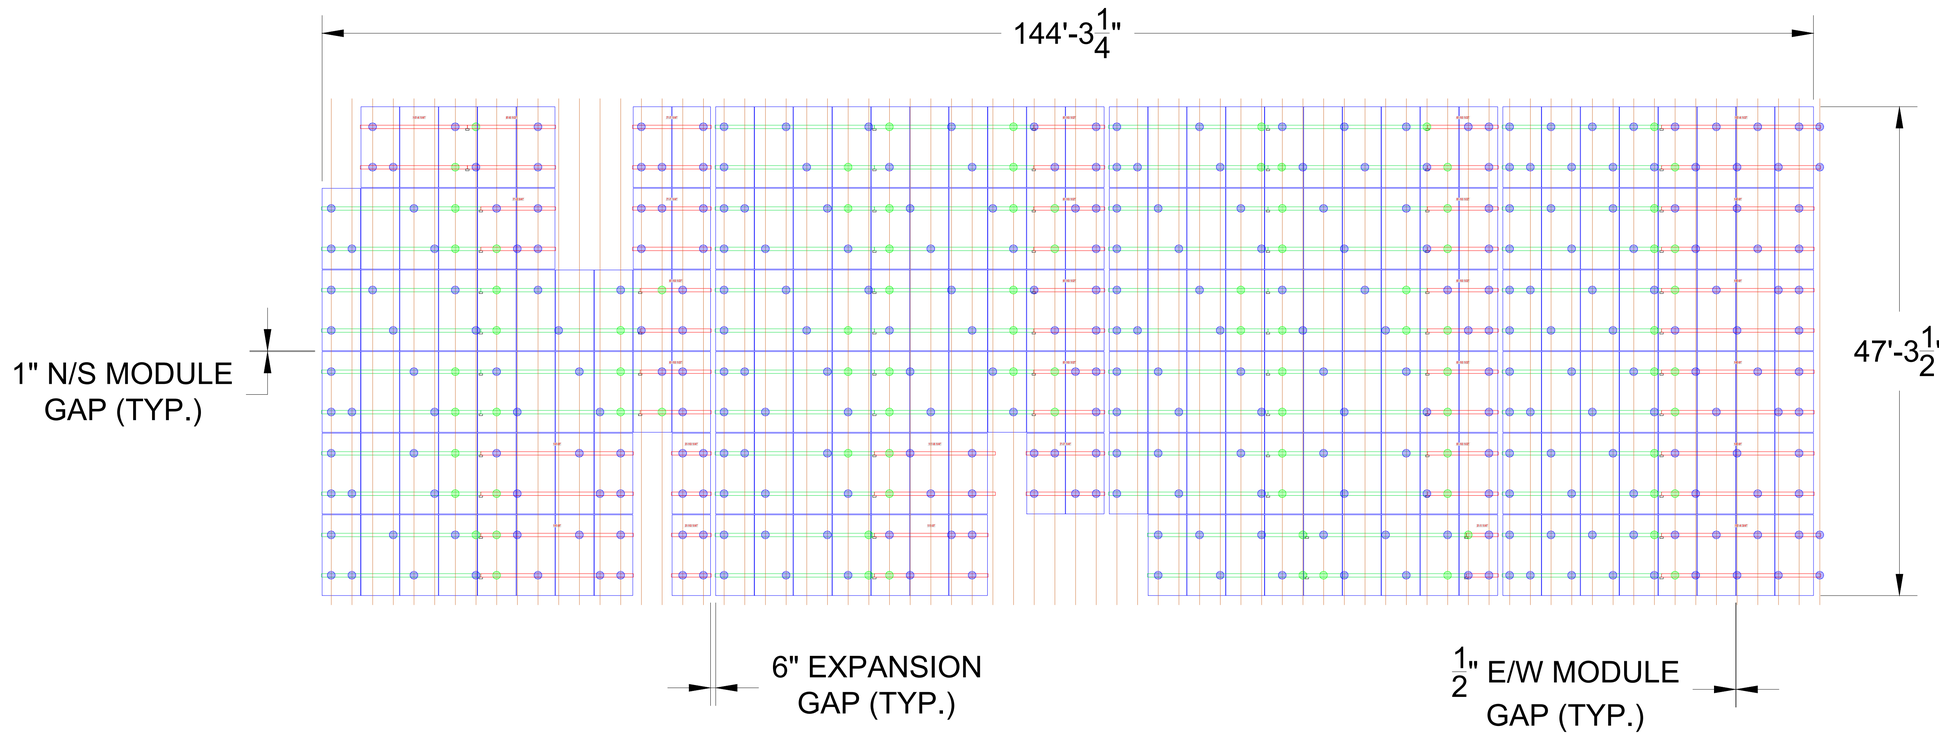

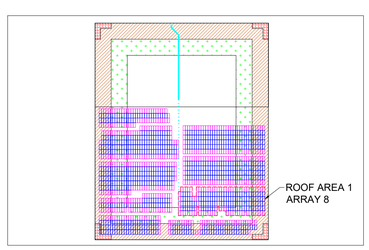

KEY PLAN
NOT TO SCALE

PLAN NORTH

NOT TO SCALE

ENGINEER'S STAMP

REVISIONS

REV	DATE	DESCRIPTION	DRW	CHK
0	01/27/2026	INITIAL RELEASE	MR	NT
A	02/02/2026	UPDATED PRODUCT	MR	NT
B	04/08/2026	UPDATED ATTACHMENT	SK	SK
-	-	-	-	-
-	-	-	-	-
-	-	-	-	-
-	-	-	-	-
-	-	-	-	-
-	-	-	-	-

FOR

PROJECT

TITLE

ARRAY LAYOUT
ROOF AREA 1
ARRAY 8

SHEET

SM.308

- 185" RAIL
- CUT-ONSITE RAIL
- #'- # #" - CUT-ONSITE RAIL LENGTH
- S5! ATTACHMENT
- S5! ATTACHMENT
- RAFTER @24"O.C.
- SPLICE BAR(TYP.)

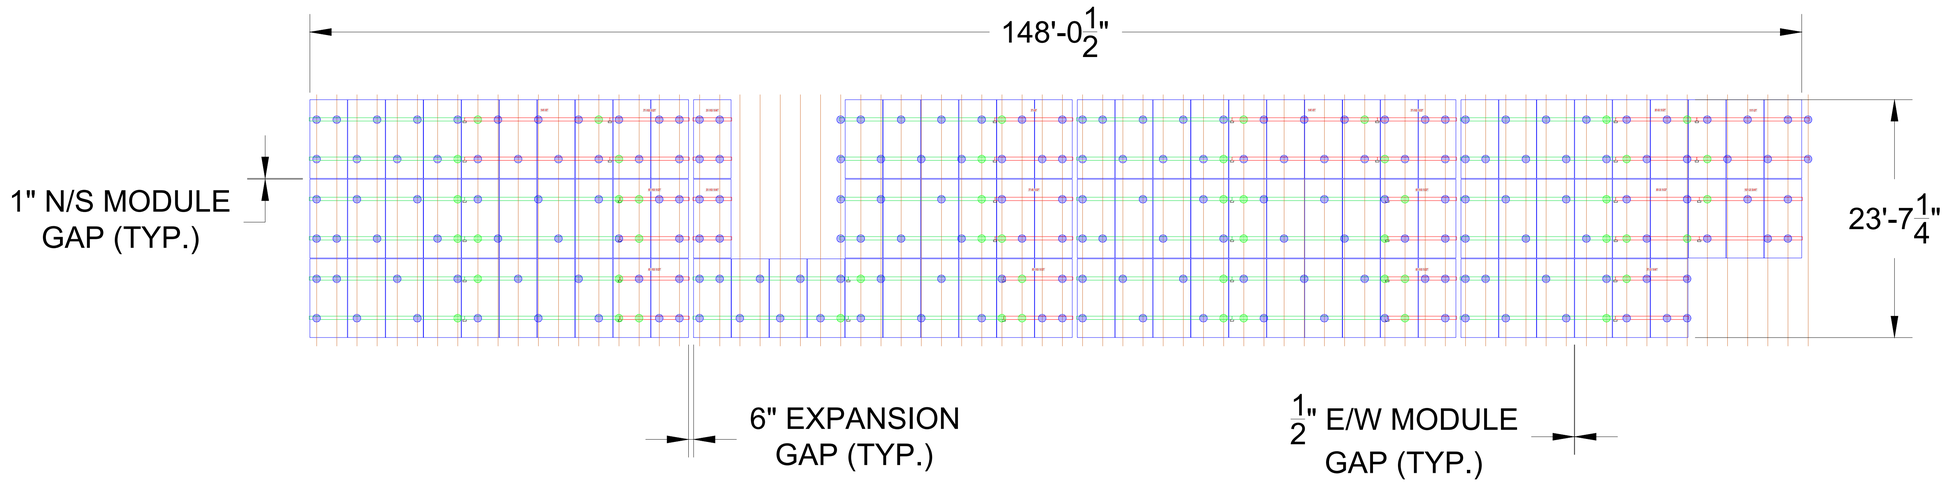

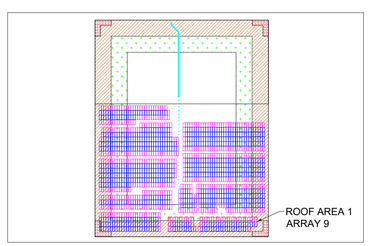

KEY PLAN
NOT TO SCALE

PLAN NORTH

NOT TO SCALE

ENGINEER'S STAMP

REVISIONS

REV	DATE	DESCRIPTION	DRW	CHK
0	01/27/2026	INITIAL RELEASE	MR	NT
A	02/02/2026	UPDATED PRODUCT	MR	NT
B	04/08/2026	UPDATED ATTACHMENT	SK	SK
-	-	-	-	-
-	-	-	-	-
-	-	-	-	-
-	-	-	-	-
-	-	-	-	-
-	-	-	-	-

FOR

PROJECT

TITLE

ARRAY LAYOUT
ROOF AREA 1
ARRAY 14

SHEET

SM.309