- 246" RAIL
- CUT-ONSITE RAIL
- #'- # #" - CUT-ONSITE RAIL LENGTH
- REGULAR ATTACHMENT
- RAFTER @ 96" O.C.

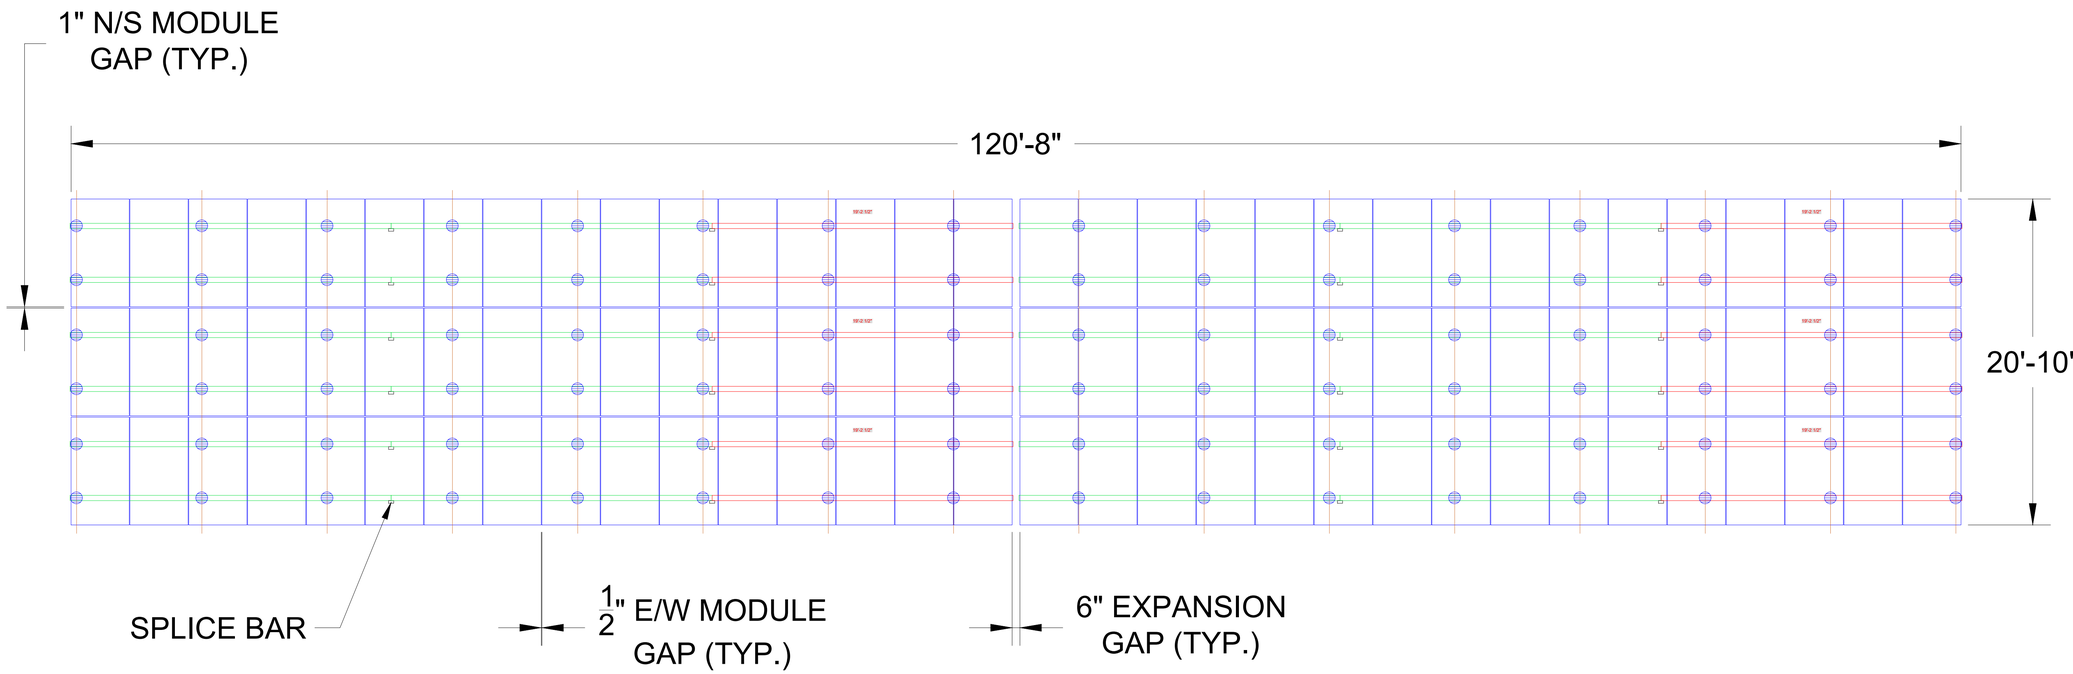

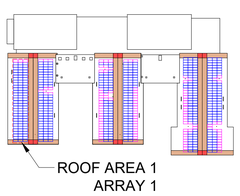

KEY PLAN
NOT TO SCALE

PLAN NORTH

NOT TO SCALE

ENGINEER'S STAMP

REVISIONS

REV	DATE	DESCRIPTION	DRW	CHK
0	12/28/2023	INITIAL RELEASE	SK	NT
A	01/08/2024	UPDATED TO DOUBLE L-FOOT	SK	NT
B	02/13/2024	UPDATED LAYOUT	SK	NT
C	03/13/2026	UPDATED LAYOUT	GC	SK
D	04/02/2026	UPDATED LAYOUT	GC	SK
-	-	-	-	-
-	-	-	-	-
-	-	-	-	-
-	-	-	-	-

FOR

PROJECT

TITLE

ARRAY LAYOUT
ROOF AREA 1
ARRAY 12

SHEET

SM.301

- 246" RAIL
- CUT-ONSITE RAIL
- #'- # #" - CUT-ONSITE RAIL LENGTH
- REGULAR ATTACHMENT
- RAFTER @ 96" O.C.

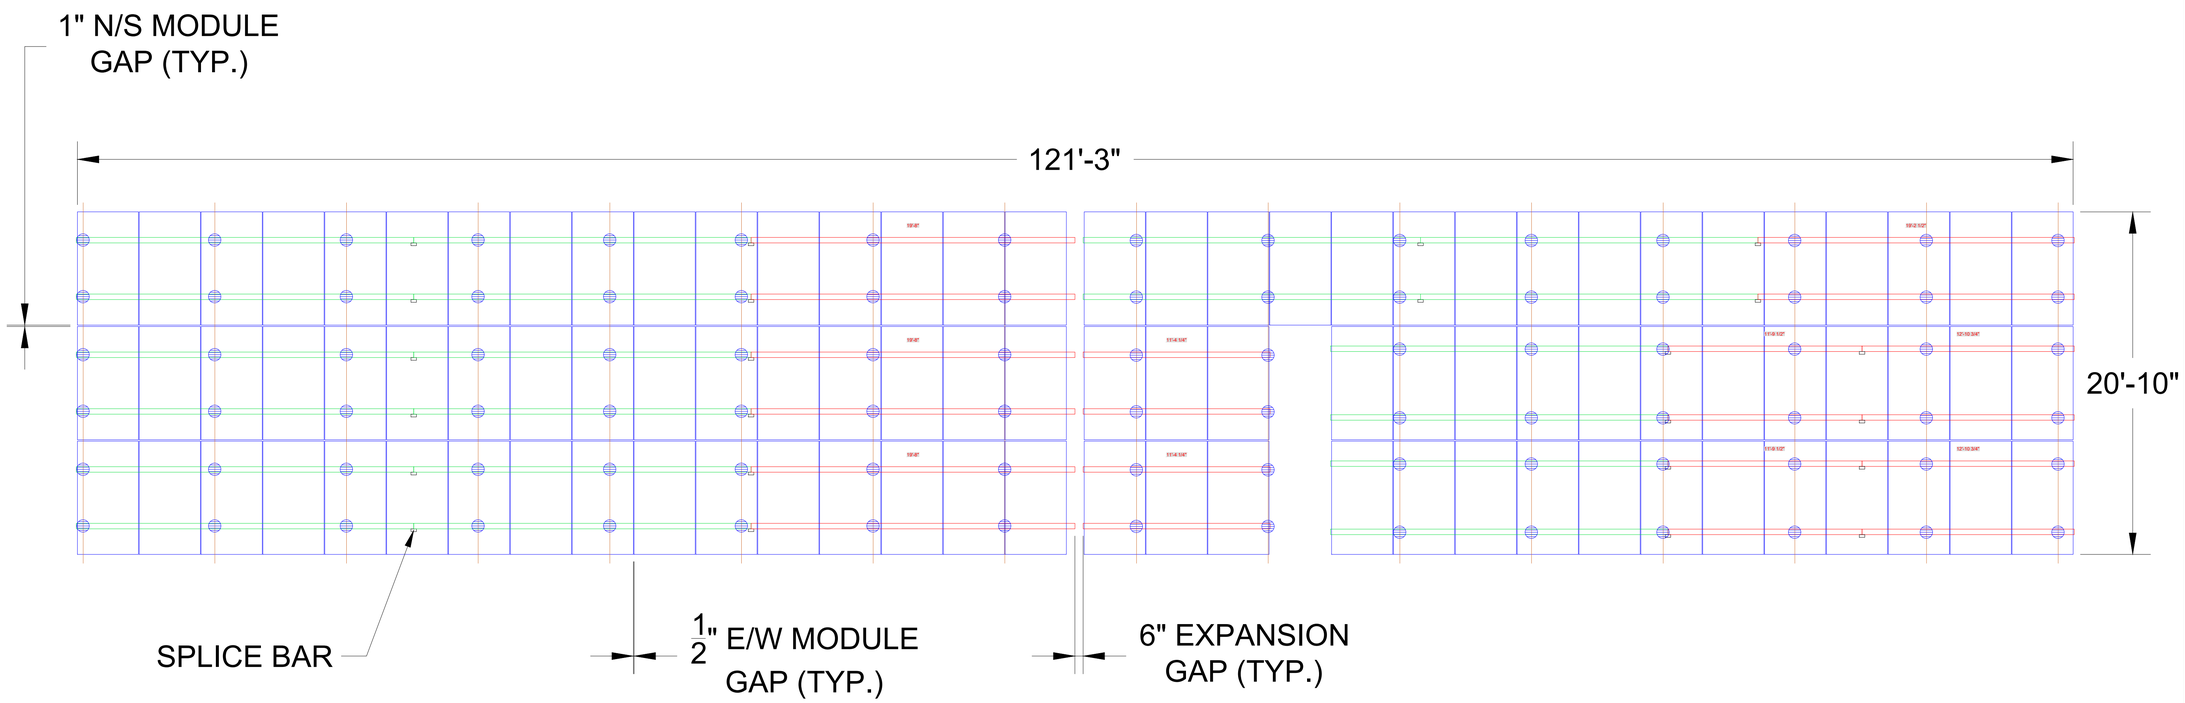

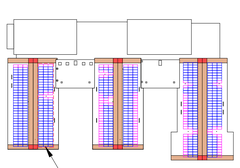

KEY PLAN
NOT TO SCALE

PLAN NORTH

NOT TO SCALE

ENGINEER'S STAMP

REVISIONS

REV	DATE	DESCRIPTION	DRW	CHK
0	12/28/2023	INITIAL RELEASE	SK	NT
A	01/08/2024	UPDATED TO DOUBLE L-FOOT	SK	NT
B	02/13/2024	UPDATED LAYOUT	SK	NT
C	03/13/2026	UPDATED LAYOUT	GC	SK
D	04/02/2026	UPDATED LAYOUT	GC	SK
-	-	-	-	-
-	-	-	-	-
-	-	-	-	-
-	-	-	-	-

FOR

PROJECT

TITLE

ARRAY LAYOUT
ROOF AREA 1
ARRAY 1

SHEET

SM.302

- 246" RAIL
- CUT-ONSITE RAIL
- #'- # #" - CUT-ONSITE RAIL LENGTH
- REGULAR ATTACHMENT
- RAFTER @ 96" O.C.

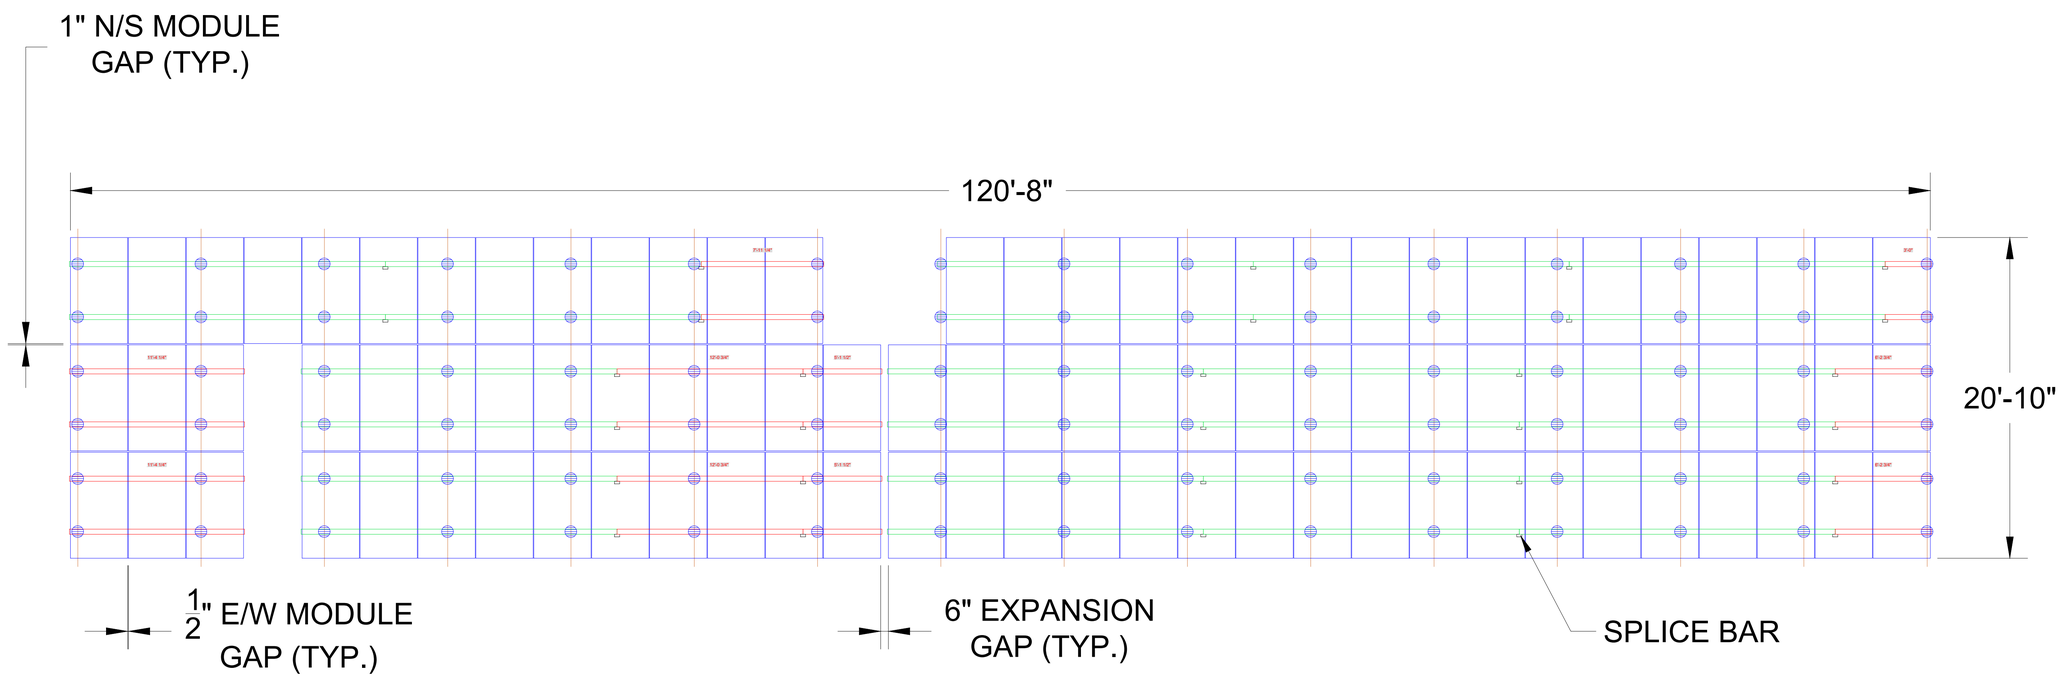

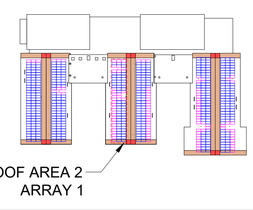

KEY PLAN
NOT TO SCALE

PLAN NORTH

NOT TO SCALE

ENGINEER'S STAMP

REVISIONS

REV	DATE	DESCRIPTION	DRW	CHK
0	12/28/2023	INITIAL RELEASE	SK	NT
A	01/08/2024	UPDATED TO DOUBLE L-FOOT	SK	NT
B	02/13/2024	UPDATED LAYOUT	SK	NT
C	03/13/2026	UPDATED LAYOUT	GC	SK
D	04/02/2026	UPDATED LAYOUT	GC	SK
-	-	-	-	-
-	-	-	-	-
-	-	-	-	-
-	-	-	-	-

FOR

PROJECT

TITLE

ARRAY LAYOUT
ROOF AREA 23
ARRAY 1

SHEET

SM.303

- 246" RAIL
- CUT-ONSITE RAIL
- #'- # #" - CUT-ONSITE RAIL LENGTH
- REGULAR ATTACHMENT
- RAFTER @ 96" O.C.

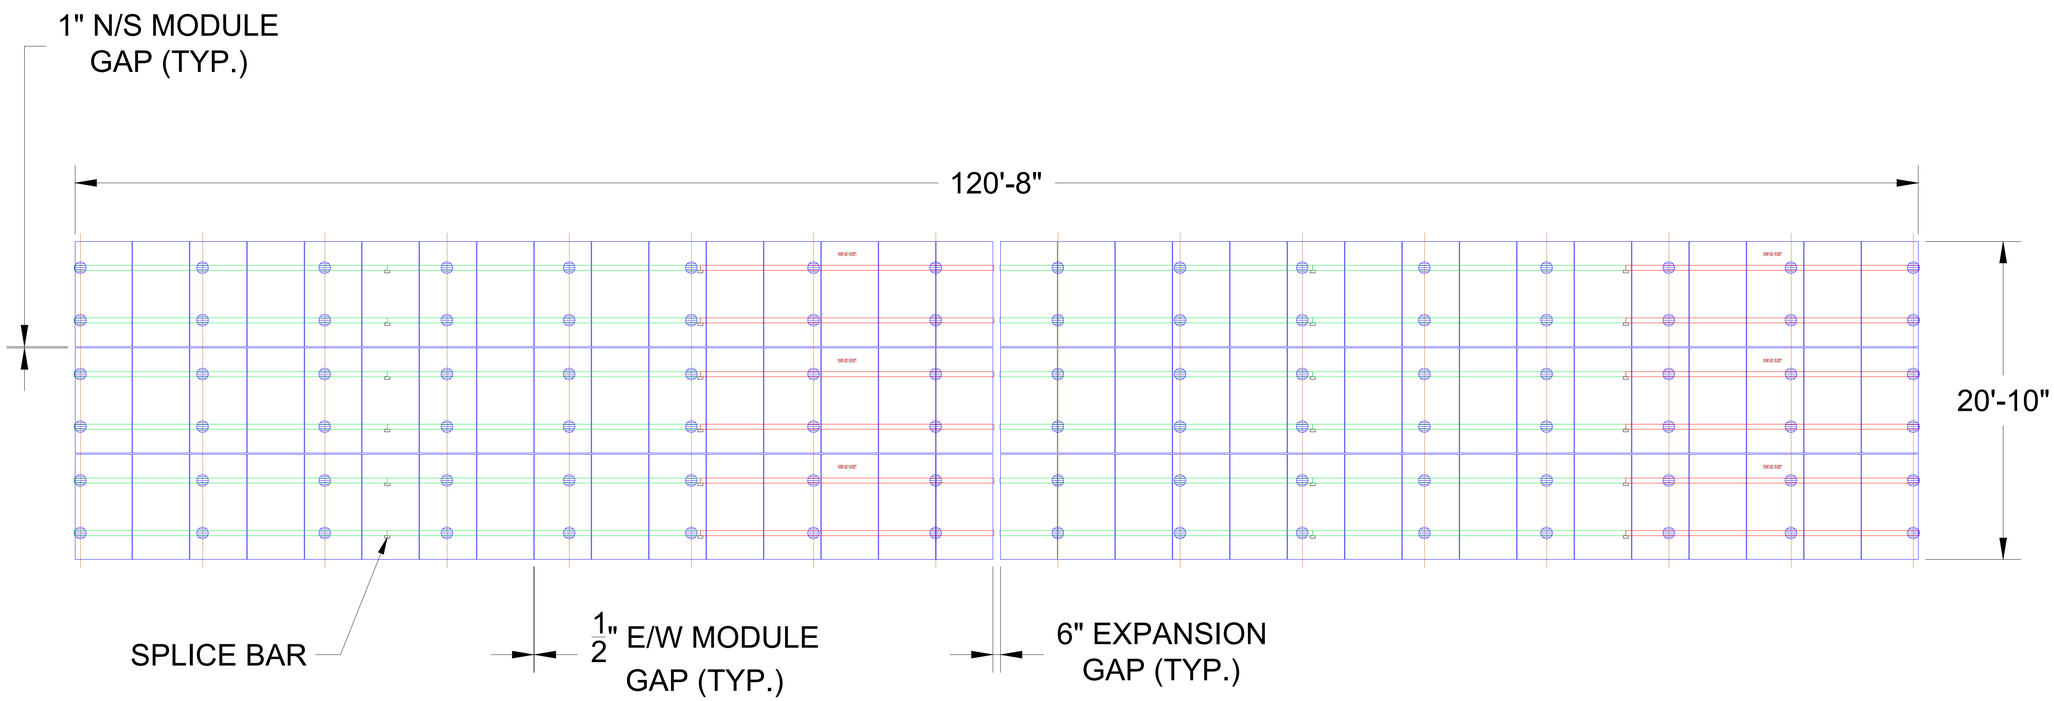

KEY PLAN
NOT TO SCALE

PLAN NORTH

NOT TO SCALE

ENGINEER'S STAMP

REVISIONS

REV	DATE	DESCRIPTION	DRW	CHK
0	12/28/2023	INITIAL RELEASE	SK	NT
A	01/08/2024	UPDATED TO DOUBLE L-FOOT	SK	NT
B	02/13/2024	UPDATED LAYOUT	SK	NT
C	03/13/2026	UPDATED LAYOUT	GC	SK
D	04/02/2026	UPDATED LAYOUT	GC	SK
-	-	-	-	-
-	-	-	-	-
-	-	-	-	-
-	-	-	-	-

FOR

PROJECT

TITLE

ARRAY LAYOUT
ROOF AREA 2
ARRAY 2

SHEET

SM.304